


TWO STREETS, ONE DOOR

The densest layout, one door open and a fixed order

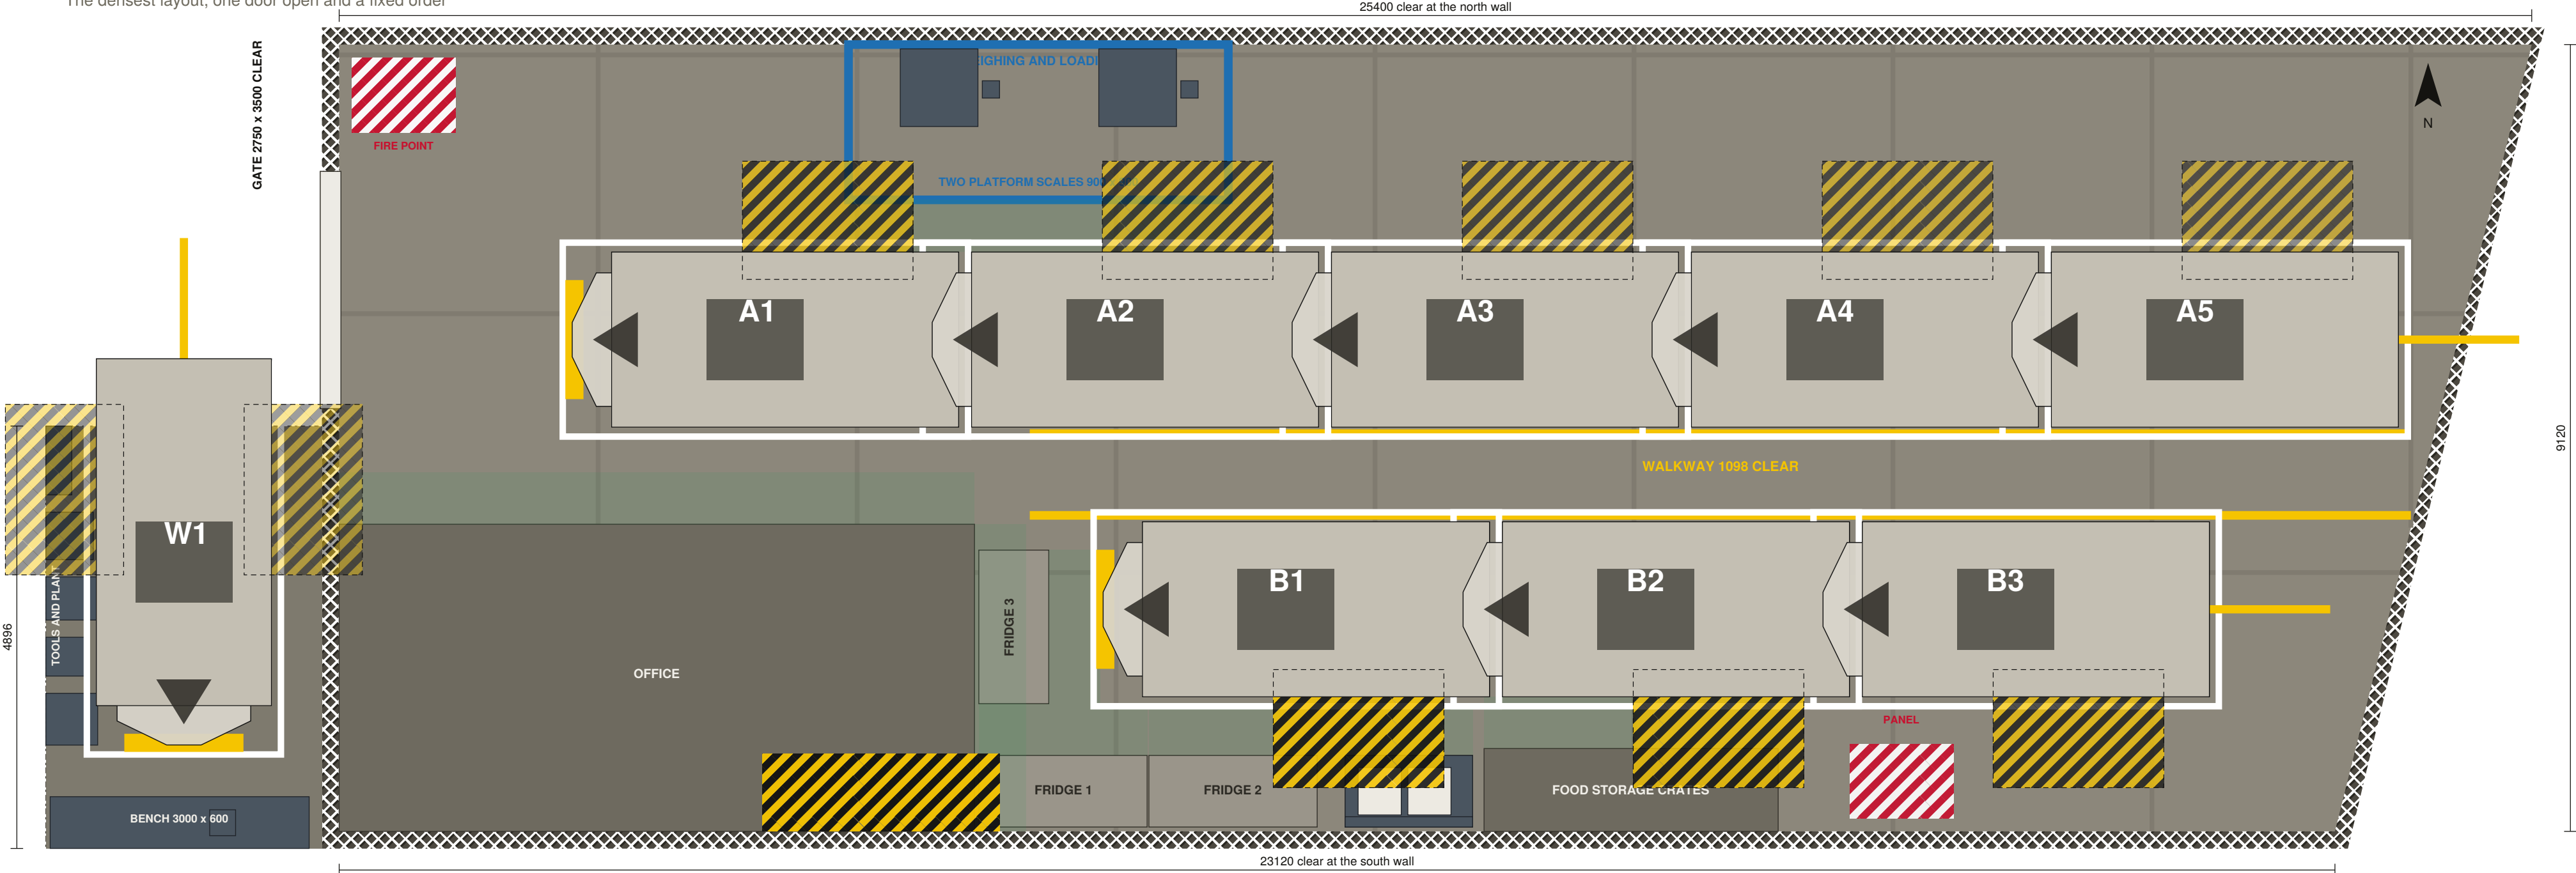

FLAGSHIPS INSIDE	8
PLUS THE WORKSHOP BAY	1
EVERY VEHICLE OPENS	1 door, in place
STREET PITCH	4170 mm
CLEARANCE AT FITTINGS	600 mm minimum
WALKWAY BETWEEN ROWS	1098 mm
ANY VEHICLE, ANY ORDER	no, fixed order
TIGHTEST POINT DRIVING OUT	41 mm

FLOOR MARKING SCHEDULE

	Black / yellow hatch Door swing. Keep clear. 1988 mm headroom.
	Yellow 100 mm Lead-in line and traffic lane edge.
	White 75 mm Vehicle stand outline and stand number.
	Blue 100 mm Weighing and loading zone, cold chain.
	Green tint 600 mm working strip at every fitting.
	Red / white hatch Fire point and electrical panel.

DAILY SEQUENCE

- Street A fills first, east to west, doors north over the weighing zone.
- Street B next, doors south over the cold line.
- Morning: all of A out west to east, then B out east to west.
- B leaves through A's lane, so A has to be clear first.
- The north strip stays clear for weighing and loading all day.

NOTES

- Eight inside plus the workshop bay. The densest layout there is, and the reference point for what the two new constraints cost.
- One door open on each vehicle, and a fixed order in and out. Both of the review's constraints are broken here.
- Kept in the set because the difference is the whole decision: eight with one door and a fixed order, three with both doors and any order.
- 1098 mm of walkway between the two streets, a real gap rather than a painted line.
- Each nose tucks 306 mm under the canopy of the vehicle ahead, which is what puts a 4476 mm vehicle on a 4170 mm pitch.