


THREE IN, SEVEN OUT

Wave one inside, wave two in the yard, both doors open

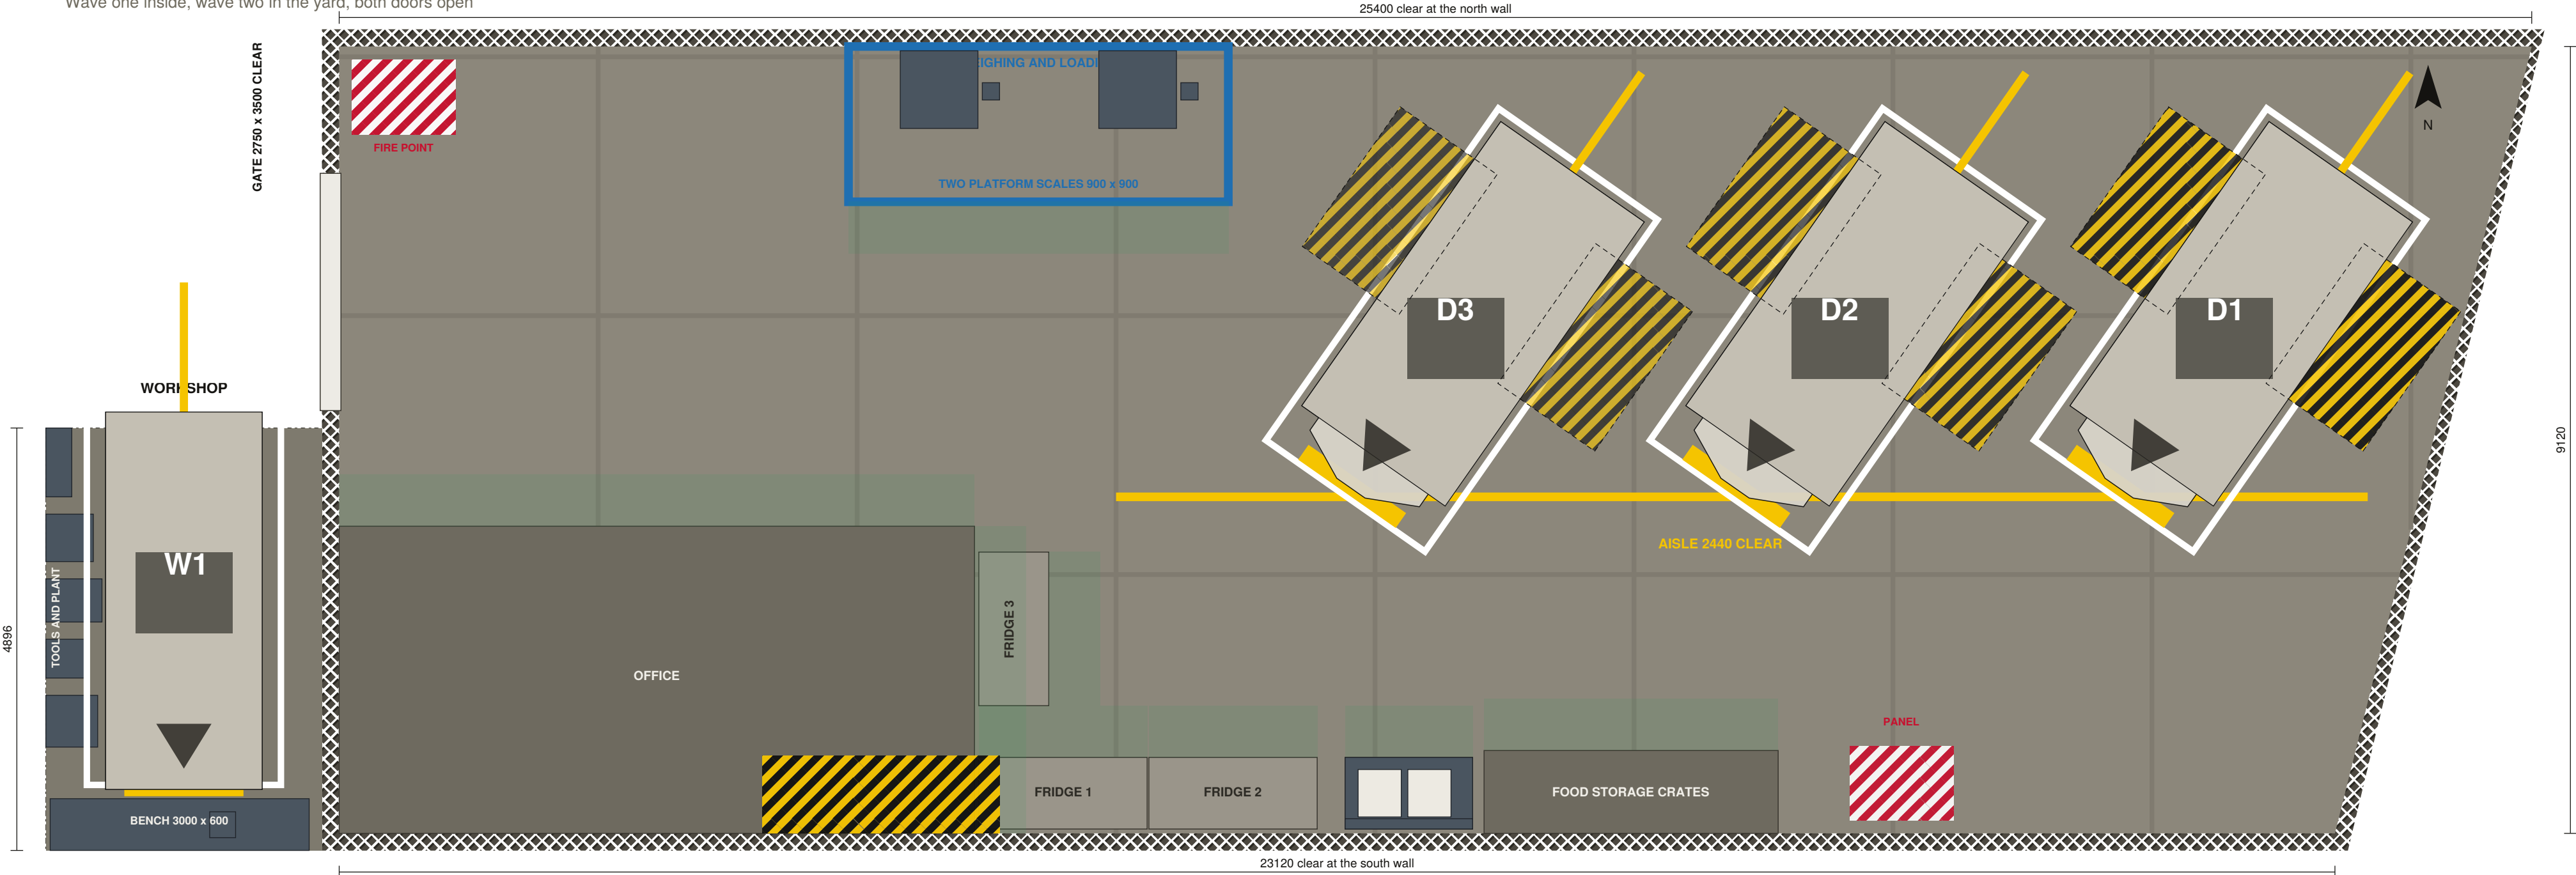

FLAGSHIPS INSIDE	3
PLUS THE WORKSHOP BAY	1
EVERY VEHICLE OPENS	both doors
STREET PITCH	4170 mm
CLEARANCE AT FITTINGS	600 mm minimum
DRIVE AISLE	2440 mm
ANY VEHICLE, ANY ORDER	yes
TIGHTEST POINT DRIVING OUT	45 mm

FLOOR MARKING SCHEDULE

	Black / yellow hatch Door swing. Keep clear. 1988 mm headroom.
	Yellow 100 mm Lead-in line and traffic lane edge.
	White 75 mm Vehicle stand outline and stand number.
	Blue 100 mm Weighing and loading zone, cold chain.
	Green tint 600 mm working strip at every fitting.
	Red / white hatch Fire point and electrical panel.

DAILY SEQUENCE

- Overnight: three Flagships inside on the diagonal, the farm vehicle in the workshop bay.
- The other seven stand in the yard, west of the workshop, both doors open.
- Morning: the three inside load and leave, in any order.
- Three from the yard come in and take the empty stands.
- Repeat. Bring the second shift of operators in as the first leaves.

NOTES

- Three inside plus the farm vehicle in the workshop bay, and seven in the yard: ten vehicles, both doors open on all of them, none of them blocking another.
- The yard is where this scheme lives or dies. Seven stands abreast with both doors open need 4285 mm of frontage each, so 30 m in one rank, or about 15 x 17 m as two ranks of four facing one aisle.
- The site model does not carry a yard boundary, so those figures are what the formation needs, not what the yard has. Chalk it out before committing.
- The turnover is the point: three go, three replace them, and the shed never has more than three loading at once. That is the constraint, not a choice.
- The farm vehicle is 4373 x 1813 x 1953 with no doors, so it parks in the workshop bay without a swing to allow for.