


TWO STREETS AND A STAGING APRON

One fewer vehicle, seven metres of clear apron at the gate

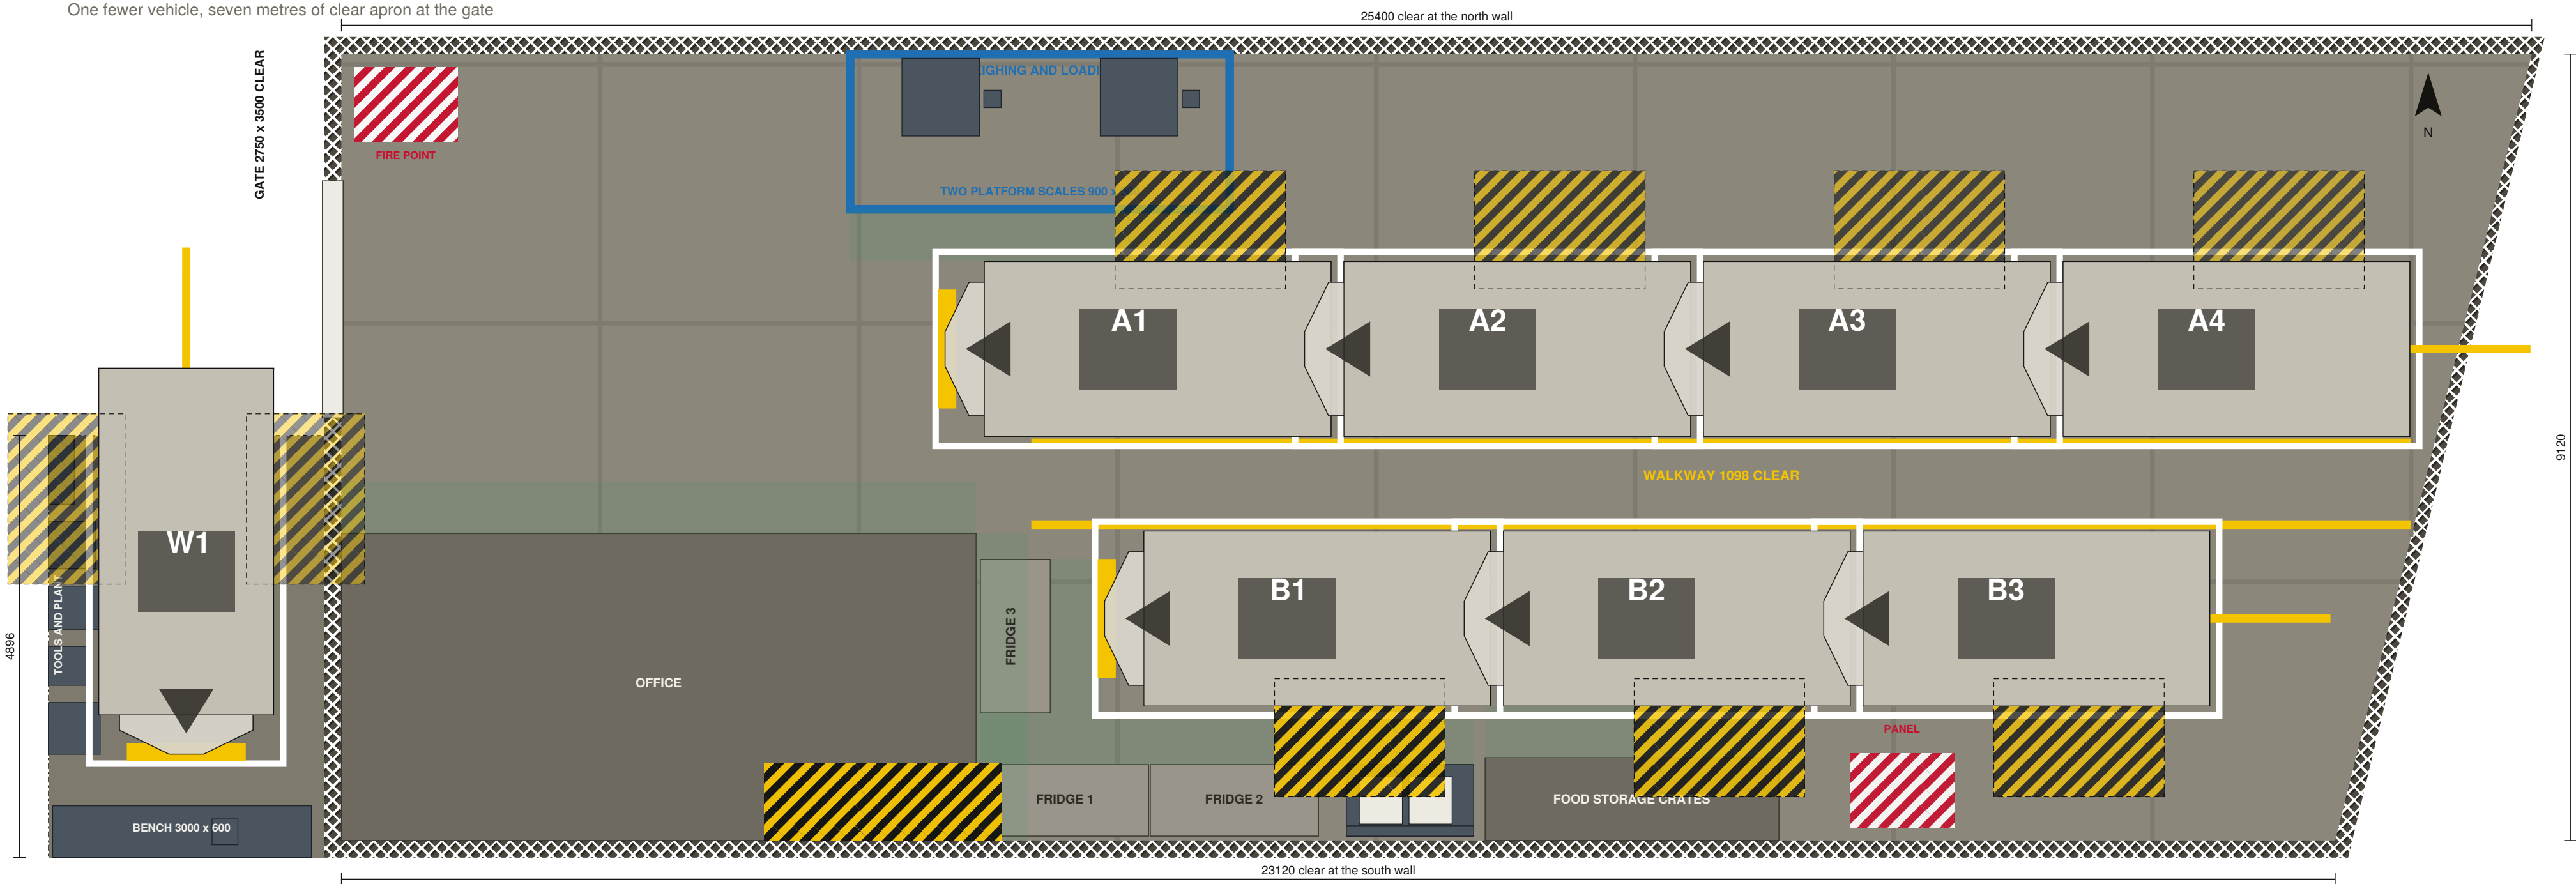

FLAGSHIPS INSIDE	7
PLUS THE WORKSHOP BAY	1
EVERY VEHICLE OPENS	1 door, in place
STREET PITCH	4170 mm
CLEARANCE AT FITTINGS	600 mm minimum
WALKWAY BETWEEN ROWS	1098 mm
TIGHTEST POINT DRIVING OUT	41 mm

FLOOR MARKING SCHEDULE

	Black / yellow hatch Door swing. Keep clear. 1988 mm headroom.
	Yellow 100 mm Lead-in line and traffic lane edge.
	White 75 mm Vehicle stand outline and stand number.
	Blue 100 mm Weighing and loading zone, cold chain.
	Green tint 600 mm working strip at every fitting.
	Red / white hatch Fire point and electrical panel.

DAILY SEQUENCE

- Street A fills first, east to west, doors north.
- Street B next, doors south over the cold line.
- Morning: all of A out, then B out east to west through A's lane.
- The west seven metres stay clear as the load and unload apron.
- Pull any vehicle onto the apron to open both doors.

NOTES

Seven inside plus the workshop bay, one fewer than Scheme 1, and much easier to live with.

The whole west end of the hall, seven metres of it, stays clear at the gate: room to turn, to stage a load, and to work on a vehicle with both doors open.

Street A is held back to u = 7000 so its lead vehicle has the run it needs to line up on the gate.

Row to row gap is still 1098 mm.

Same two chains as Scheme 1, one link shorter, and the daily order is easier to hold to.