


RANK, AISLE AND APRON

Four independent stands, and the aisle itself parked overnight

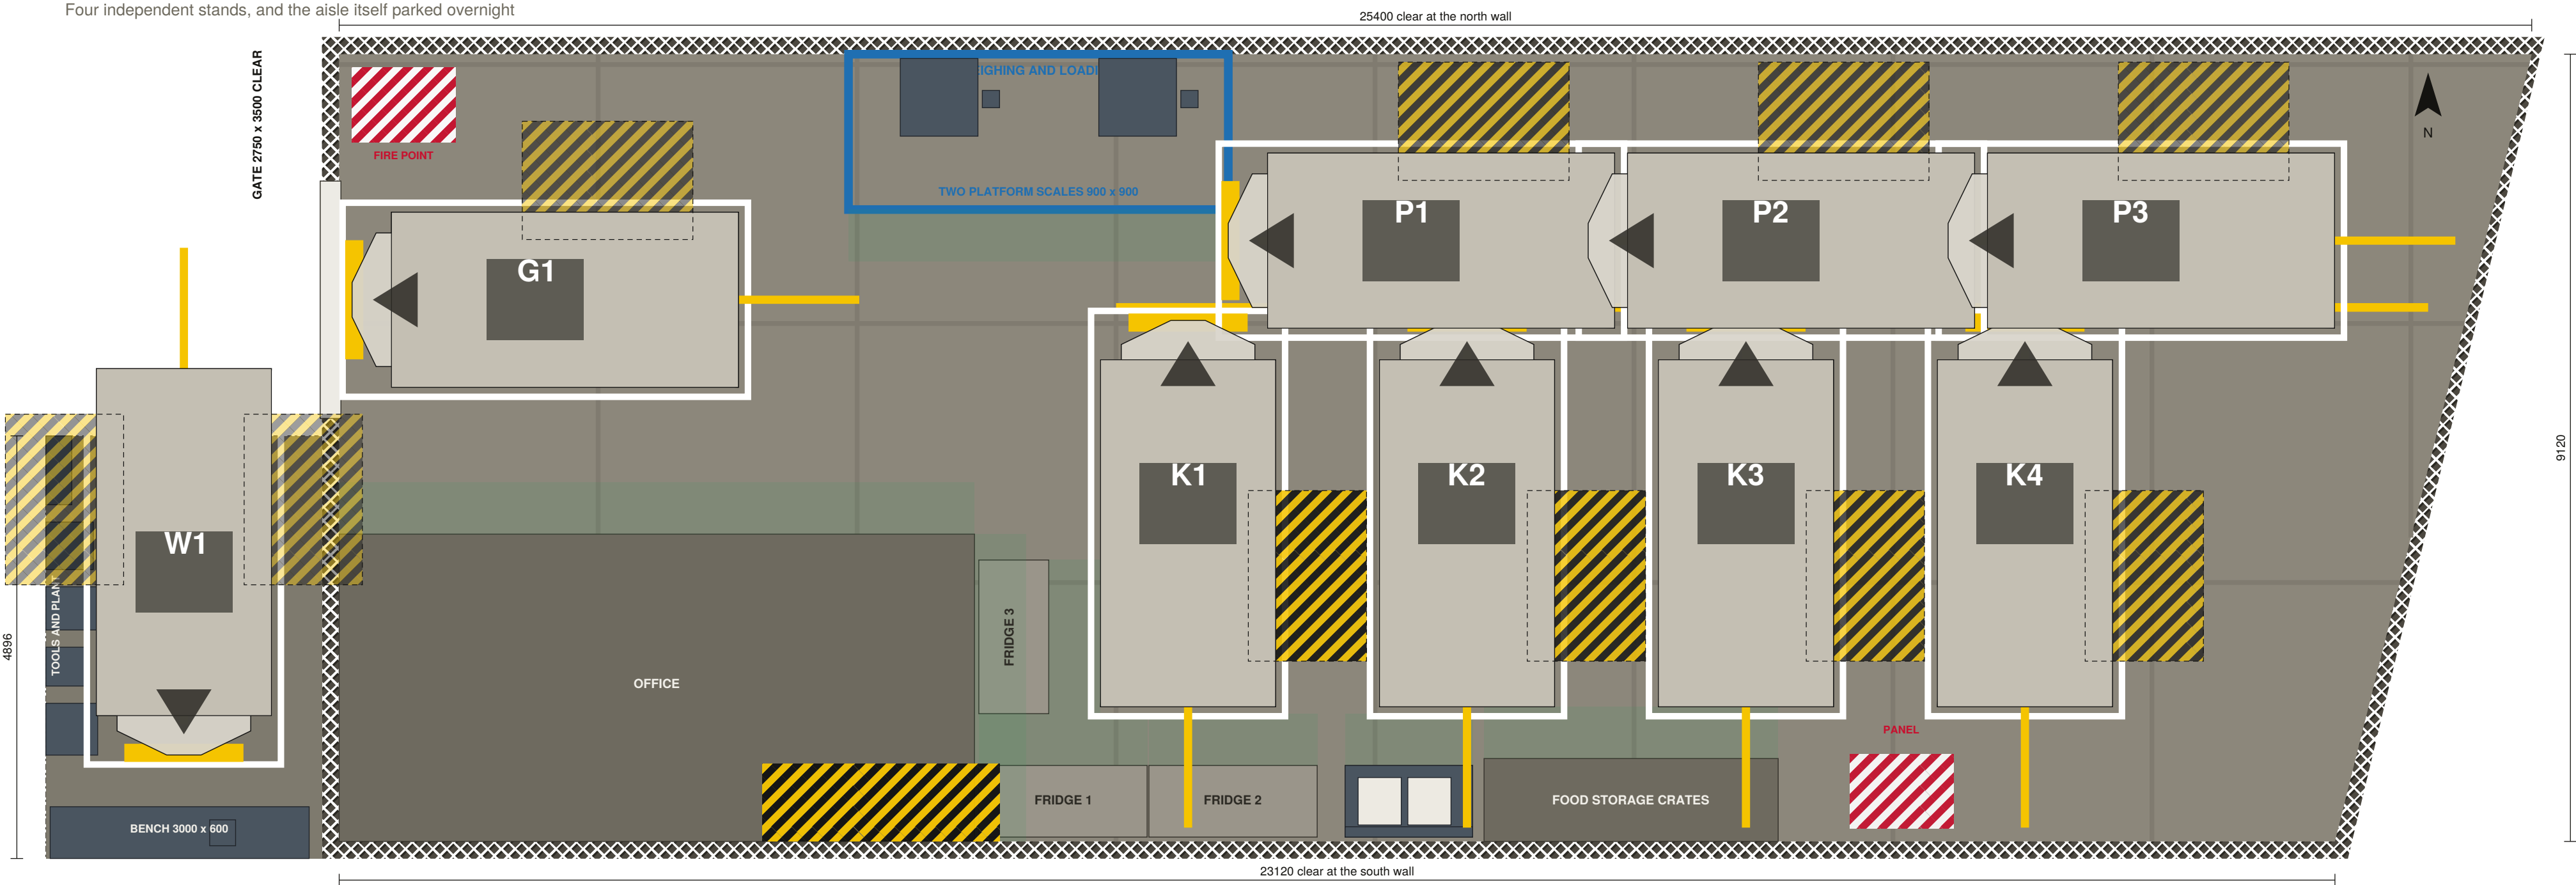

FLAGSHIPS INSIDE	8
PLUS THE WORKSHOP BAY	1
EVERY VEHICLE OPENS	1 door, in place
STREET PITCH	4170 mm
CLEARANCE AT FITTINGS	600 mm minimum
DRIVE AISLE	2934 mm
TIGHTEST POINT DRIVING OUT	58 mm

FLOOR MARKING SCHEDULE

	Black / yellow hatch Door swing. Keep clear. 1988 mm headroom.
	Yellow 100 mm Lead-in line and traffic lane edge.
	White 75 mm Vehicle stand outline and stand number.
	Blue 100 mm Weighing and loading zone, cold chain.
	Green tint 600 mm working strip at every fitting.
	Red / white hatch Fire point and electrical panel.

DAILY SEQUENCE

1. Stands K1 to K4 fill first, in any order, reversing in off the aisle.
2. P1 to P3 then stand in the aisle itself, doors north.
3. G1 goes in last, across the gate line.
4. Morning: G1 out, then K1 to K4, then P1 to P3 down the aisle.
5. By nine the aisle is clear and the scheme is Scheme 3 again.

NOTES

- Eight inside plus the workshop bay, which is the same as Scheme 1 but with four stands that stay independent.
- K1 to K4 keep their 2934 mm aisle and their nose-in stands. P1 to P3 borrow the aisle overnight, and G1 borrows the gate.
- The compromise is the aisle. While P1 to P3 are in it, the rank empties west to east instead of in any order; once they have gone the aisle is a full drive aisle again.
- The aisle row sits 150 mm off the noses of the rank and 221 mm off the scales. Paint it and fit wheel stops.
- A full length aisle plus a second nose-in row will not fit: the rank is 4476 mm deep and the aisle 2934 mm, which is 7410 mm of the 9120 mm width.